




日期				编号	图 纸 名 称	图 号	折合 张数	实际 张数	新图 纸	附 注	
											1
姓 名				1	图纸目录	-1	0.125	1	新		
				2	供电系统图	-2	0.25	1	新		
				3	供电接线图	-3	0.25	1	新		
专 业				4	保险端子接线图	-4	0.75	1	新		
				5	DI01模块接线图	-5	0.75	1	新		
日 期				6	DI02模块接线图	-6	0.75	1	新		
				7	DO01模块接线图	-7	0.5	1	新		
				8	DO02模块接线图	-8	0.5	1	新		
姓 名				9	AI模块接线图	-9	0.5	1	新		
				10	AO模块接线图	-10	0.25	1	新		
专 业				11	新图合计		4.625	10	新		
				12							
				13							
				14							
				15							
				16							
				17							
					长沙智宸自动化设备有限公司						
修改号	修改说明	修改人	修改日期		首钢京唐钢铁联合有限责任公司炼铁作业部PLC项目						
审 定			设计专业								工 程 名 称
组 审			设计阶段		子项名称	abPLC系统					
校 审			比 例		图纸名称	图纸目录					
设 计			完成日期	2026.5	图 号	-1				图幅	A4
客户图号					图 号	-1				图幅	A4

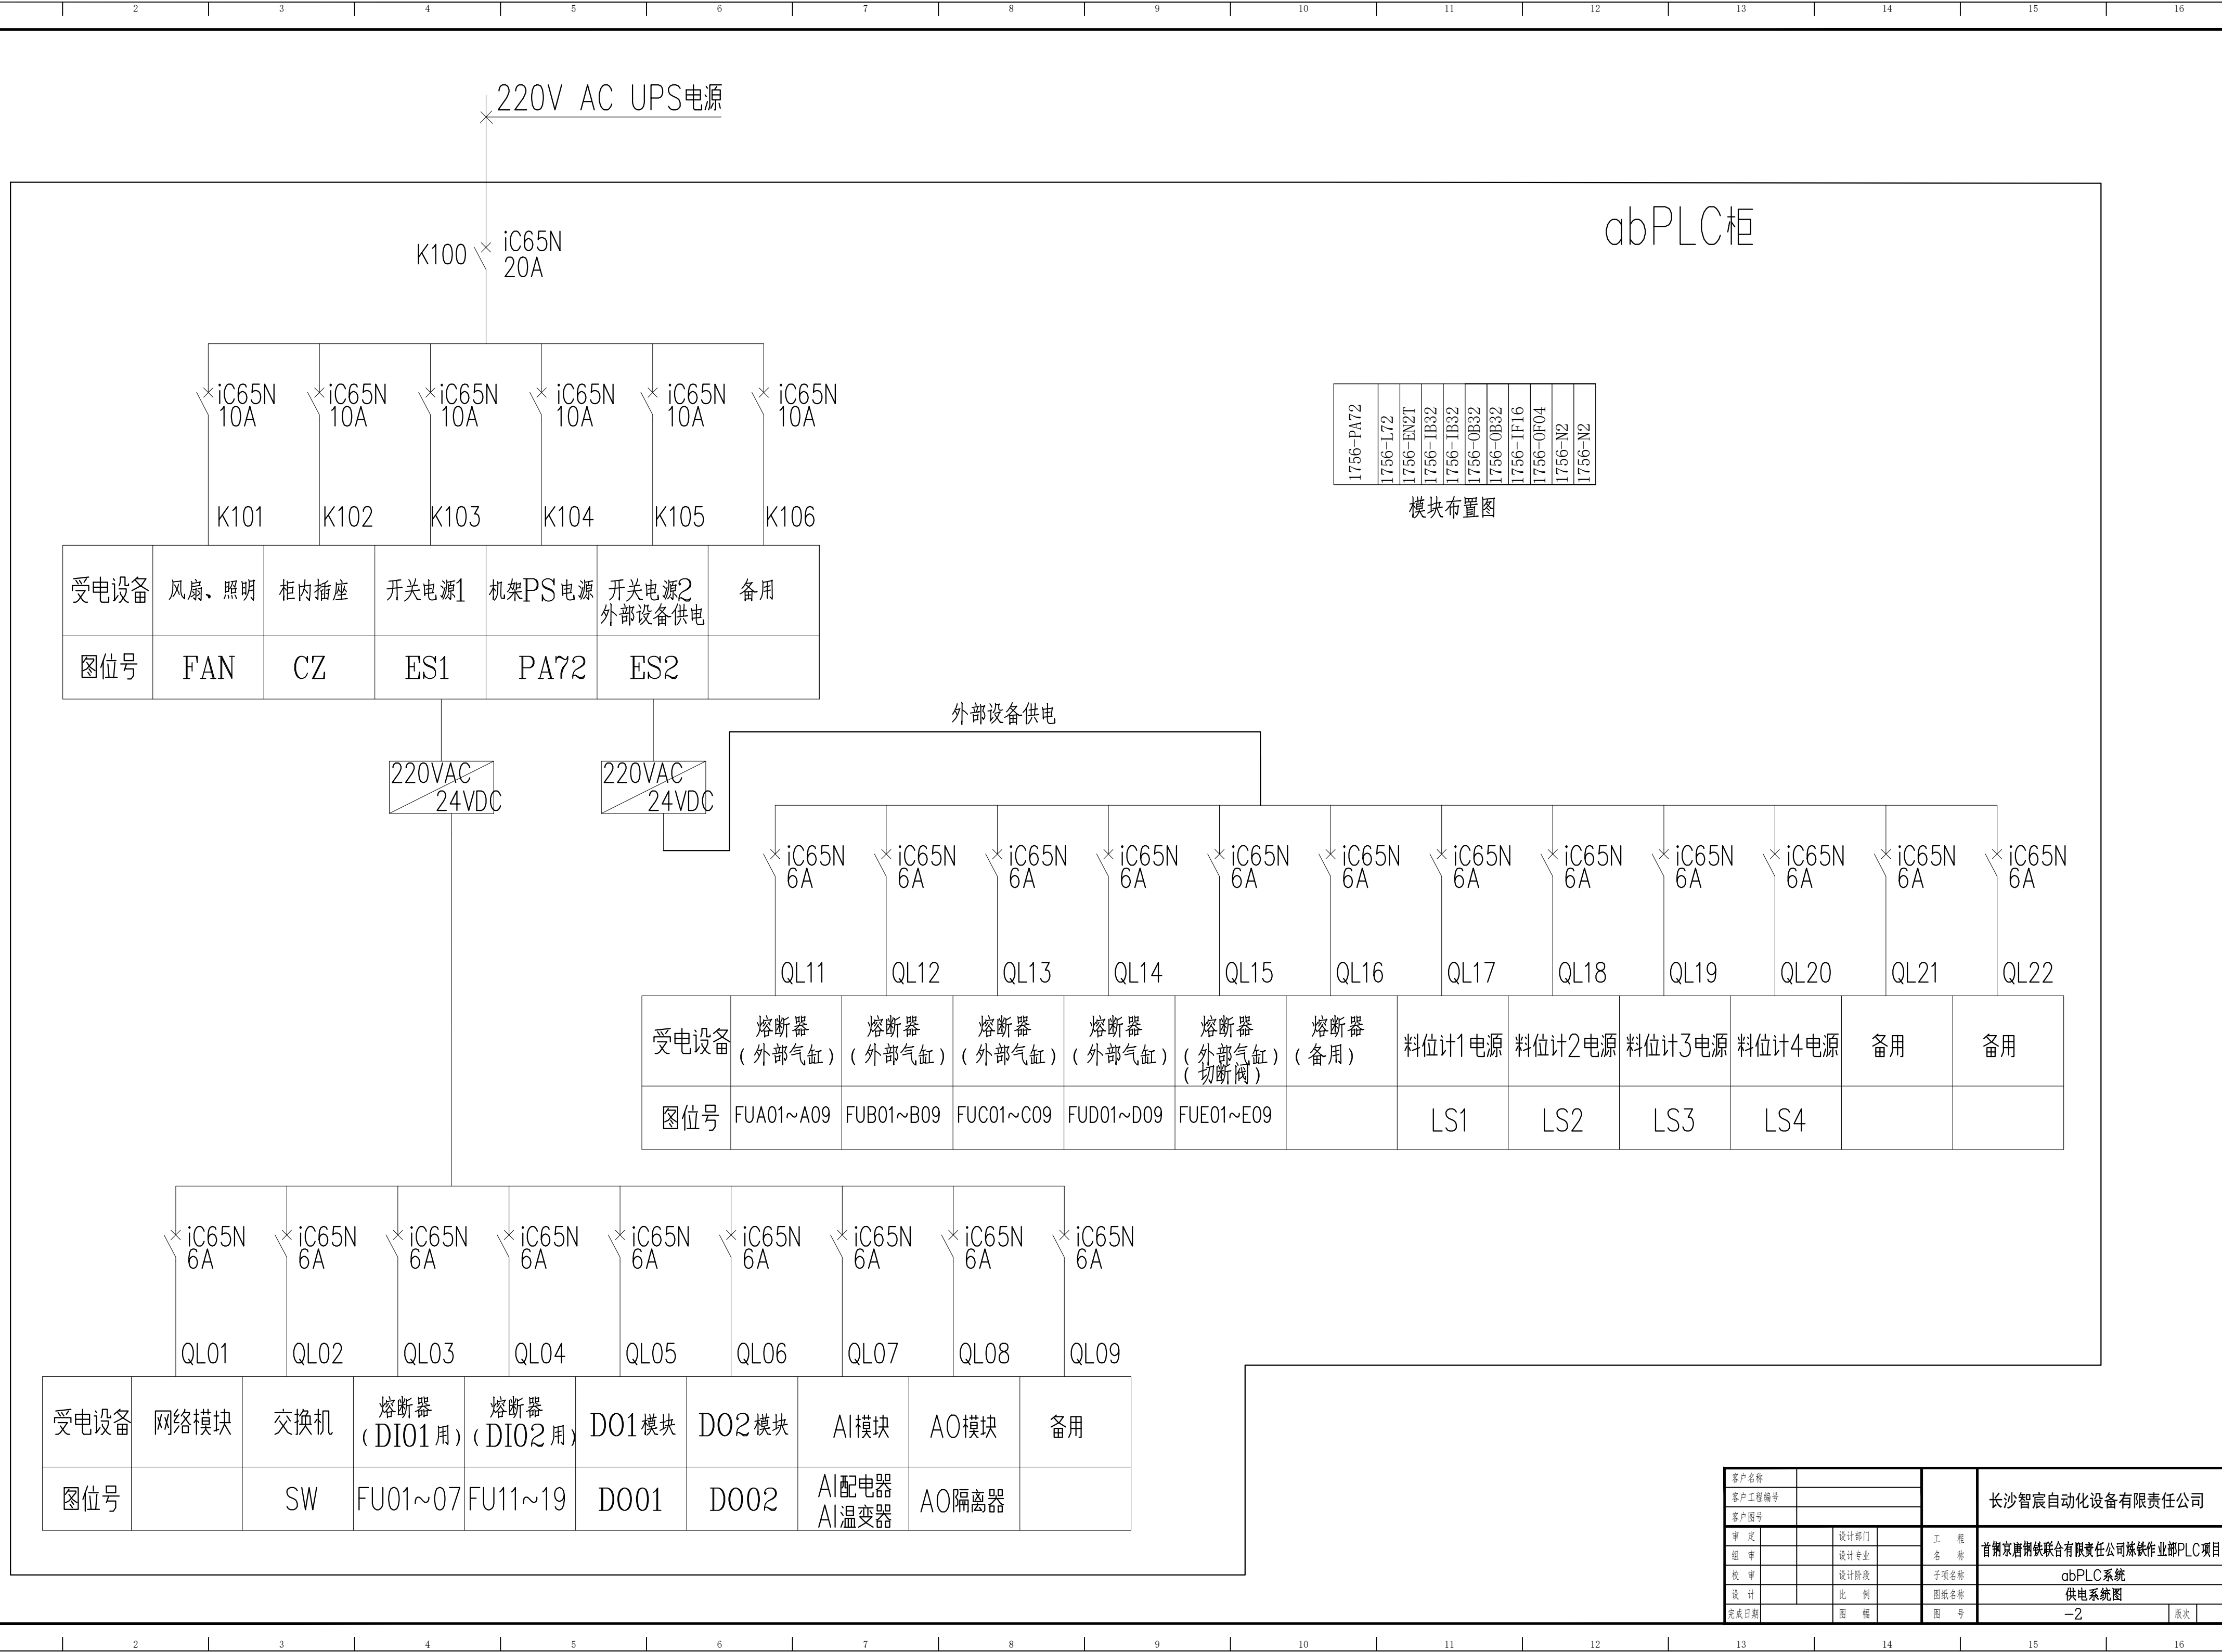



来自电源220VAC ,50Hz电源

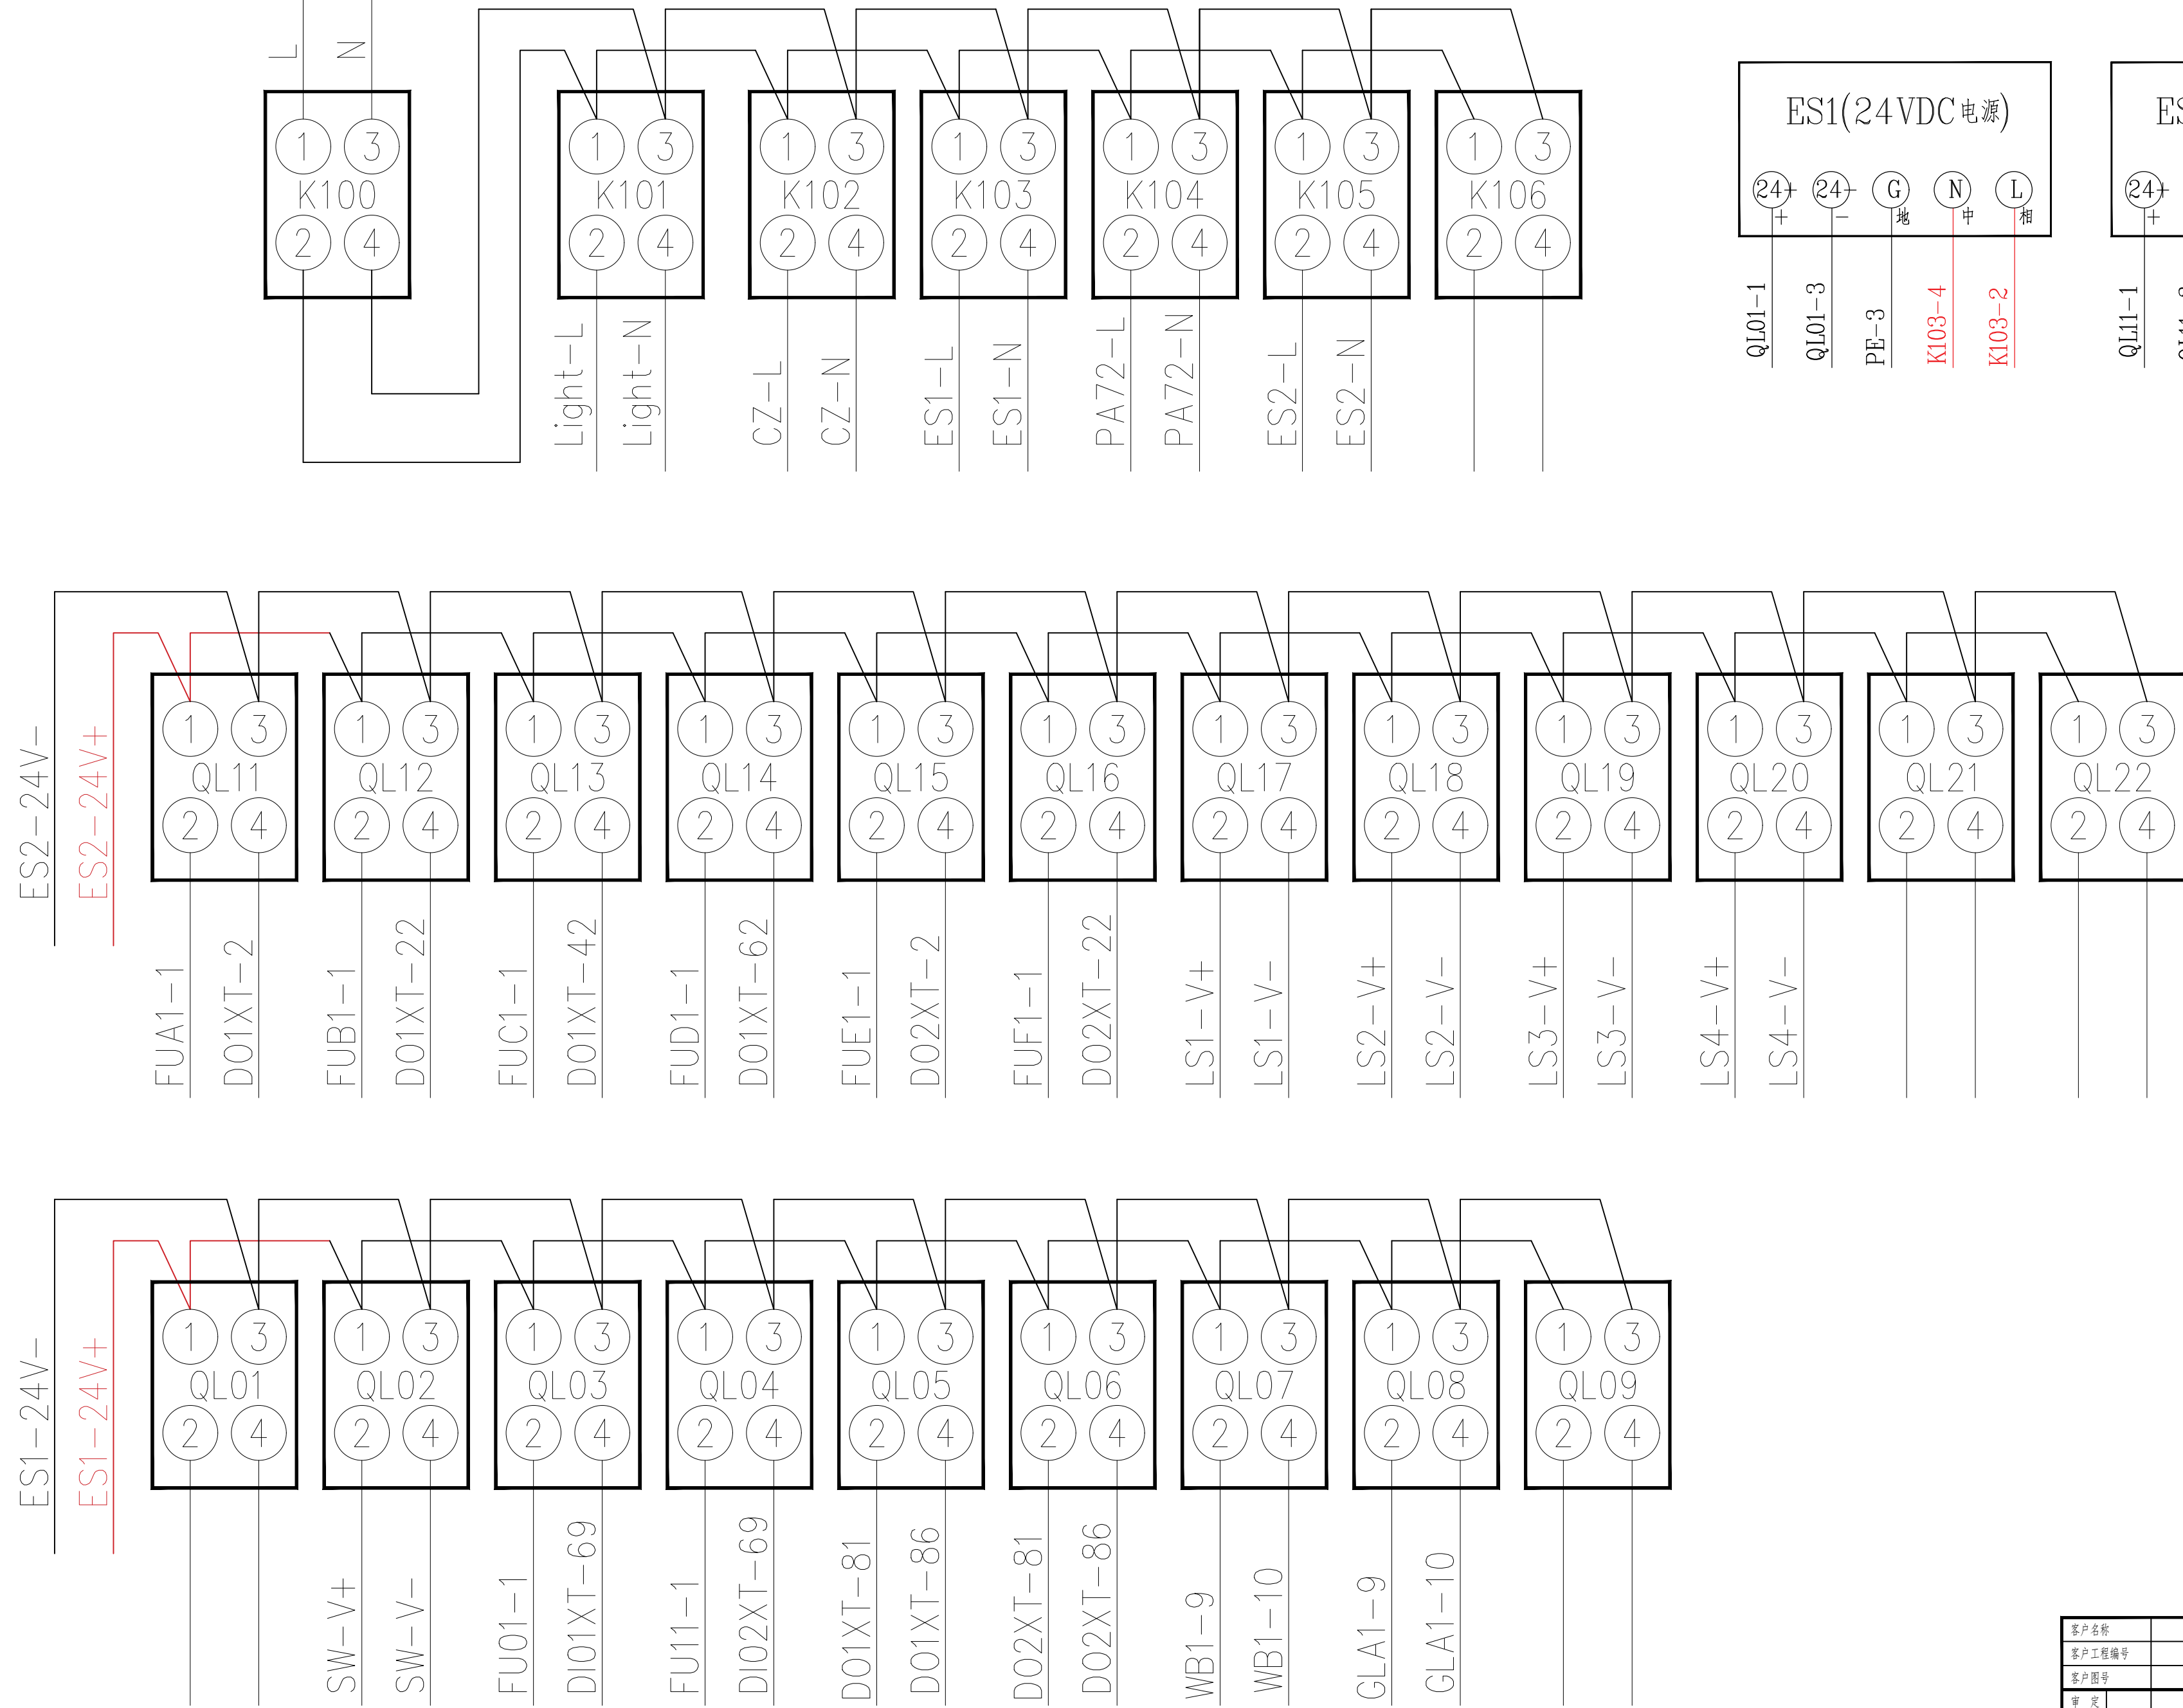


客户名称			长沙智宸自动化设备有限责任公司
客户工程编号			
客户图号			
审 定		设计部门	工 程 名 称
组 审		设计专业	首钢京唐钢铁联合有限责任公司炼铁作业部PLC项目
校 审		设计阶段	子项名称
设 计		比 例	abPLC系统
完成日期		图 幅	图纸名称
			供电接线图
			-3
			版次

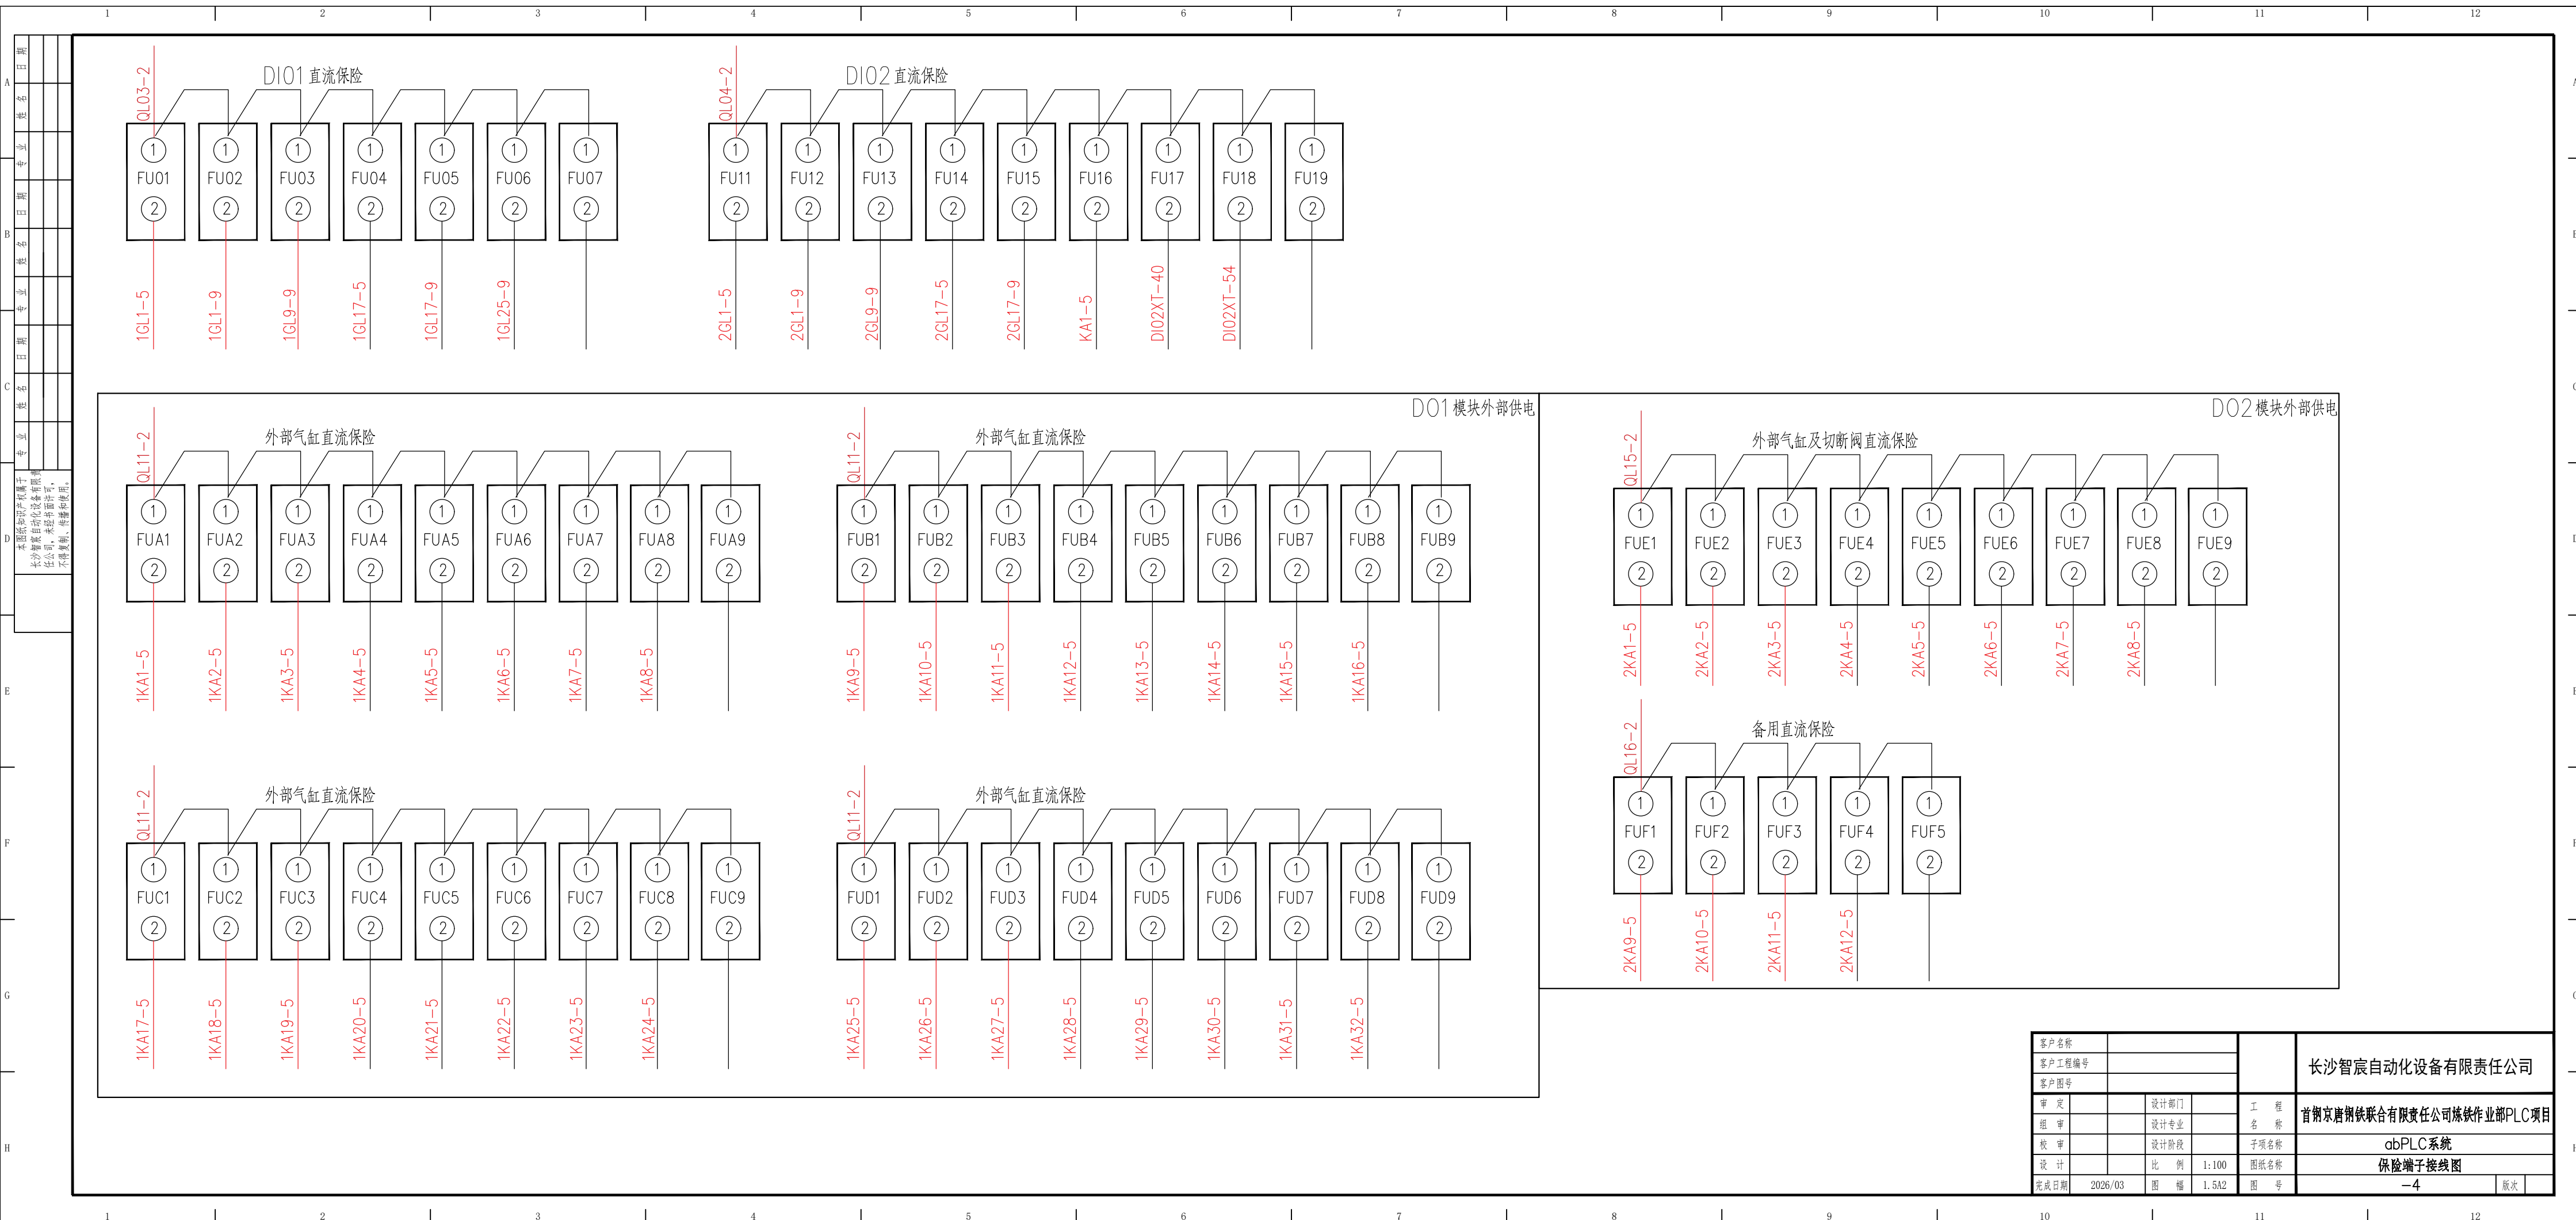

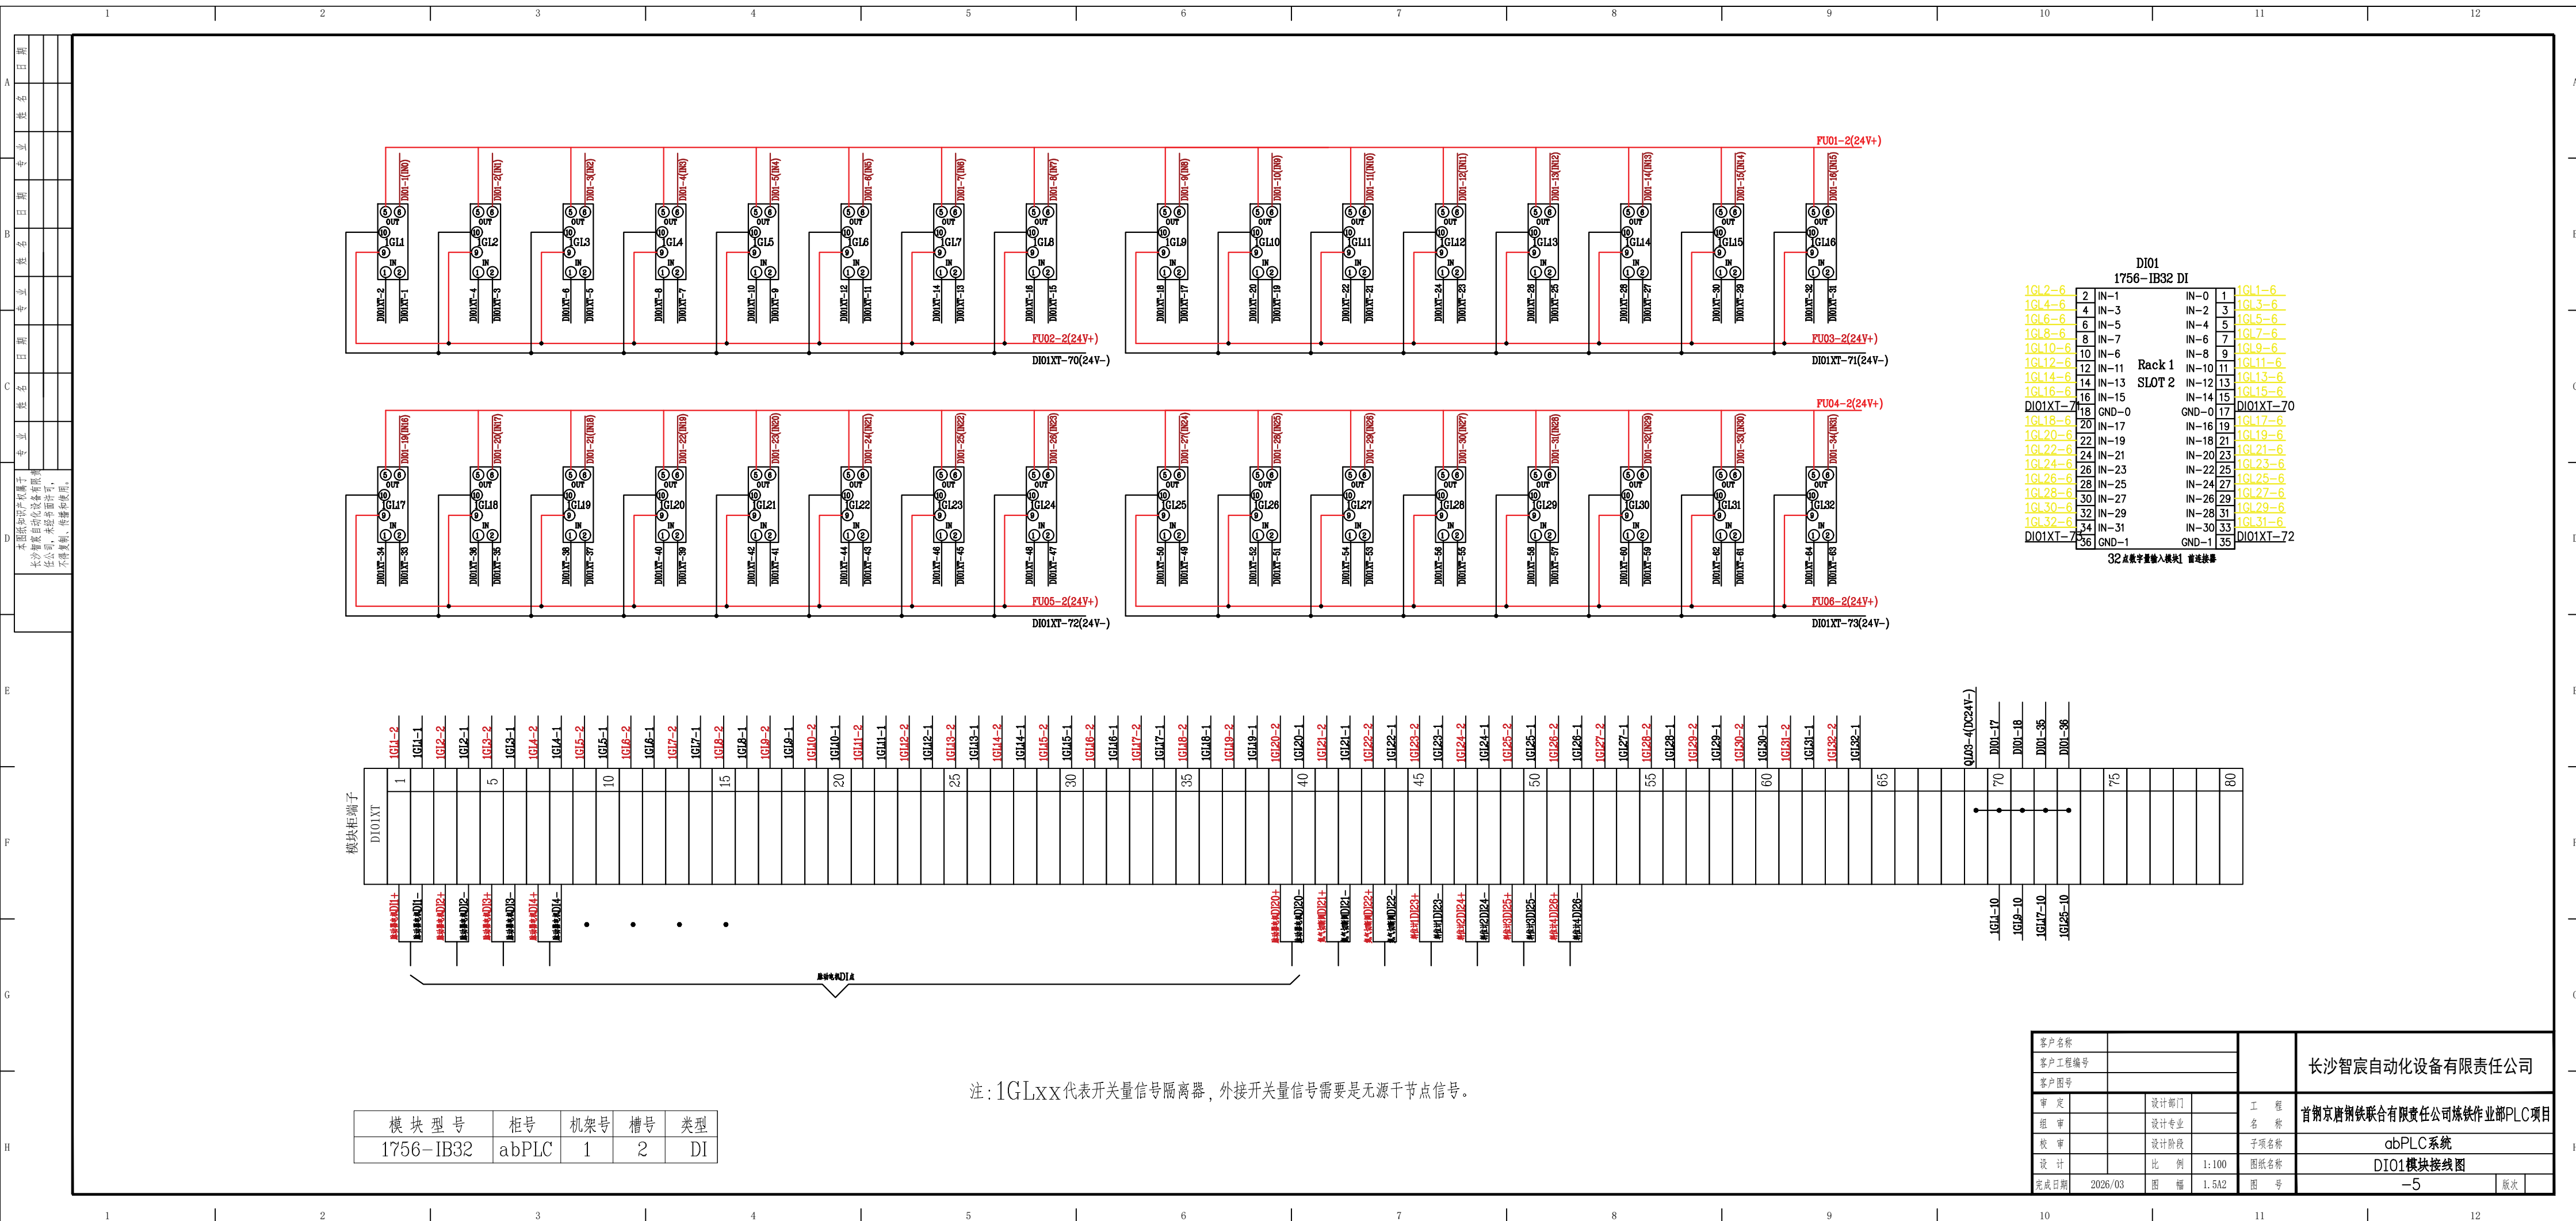

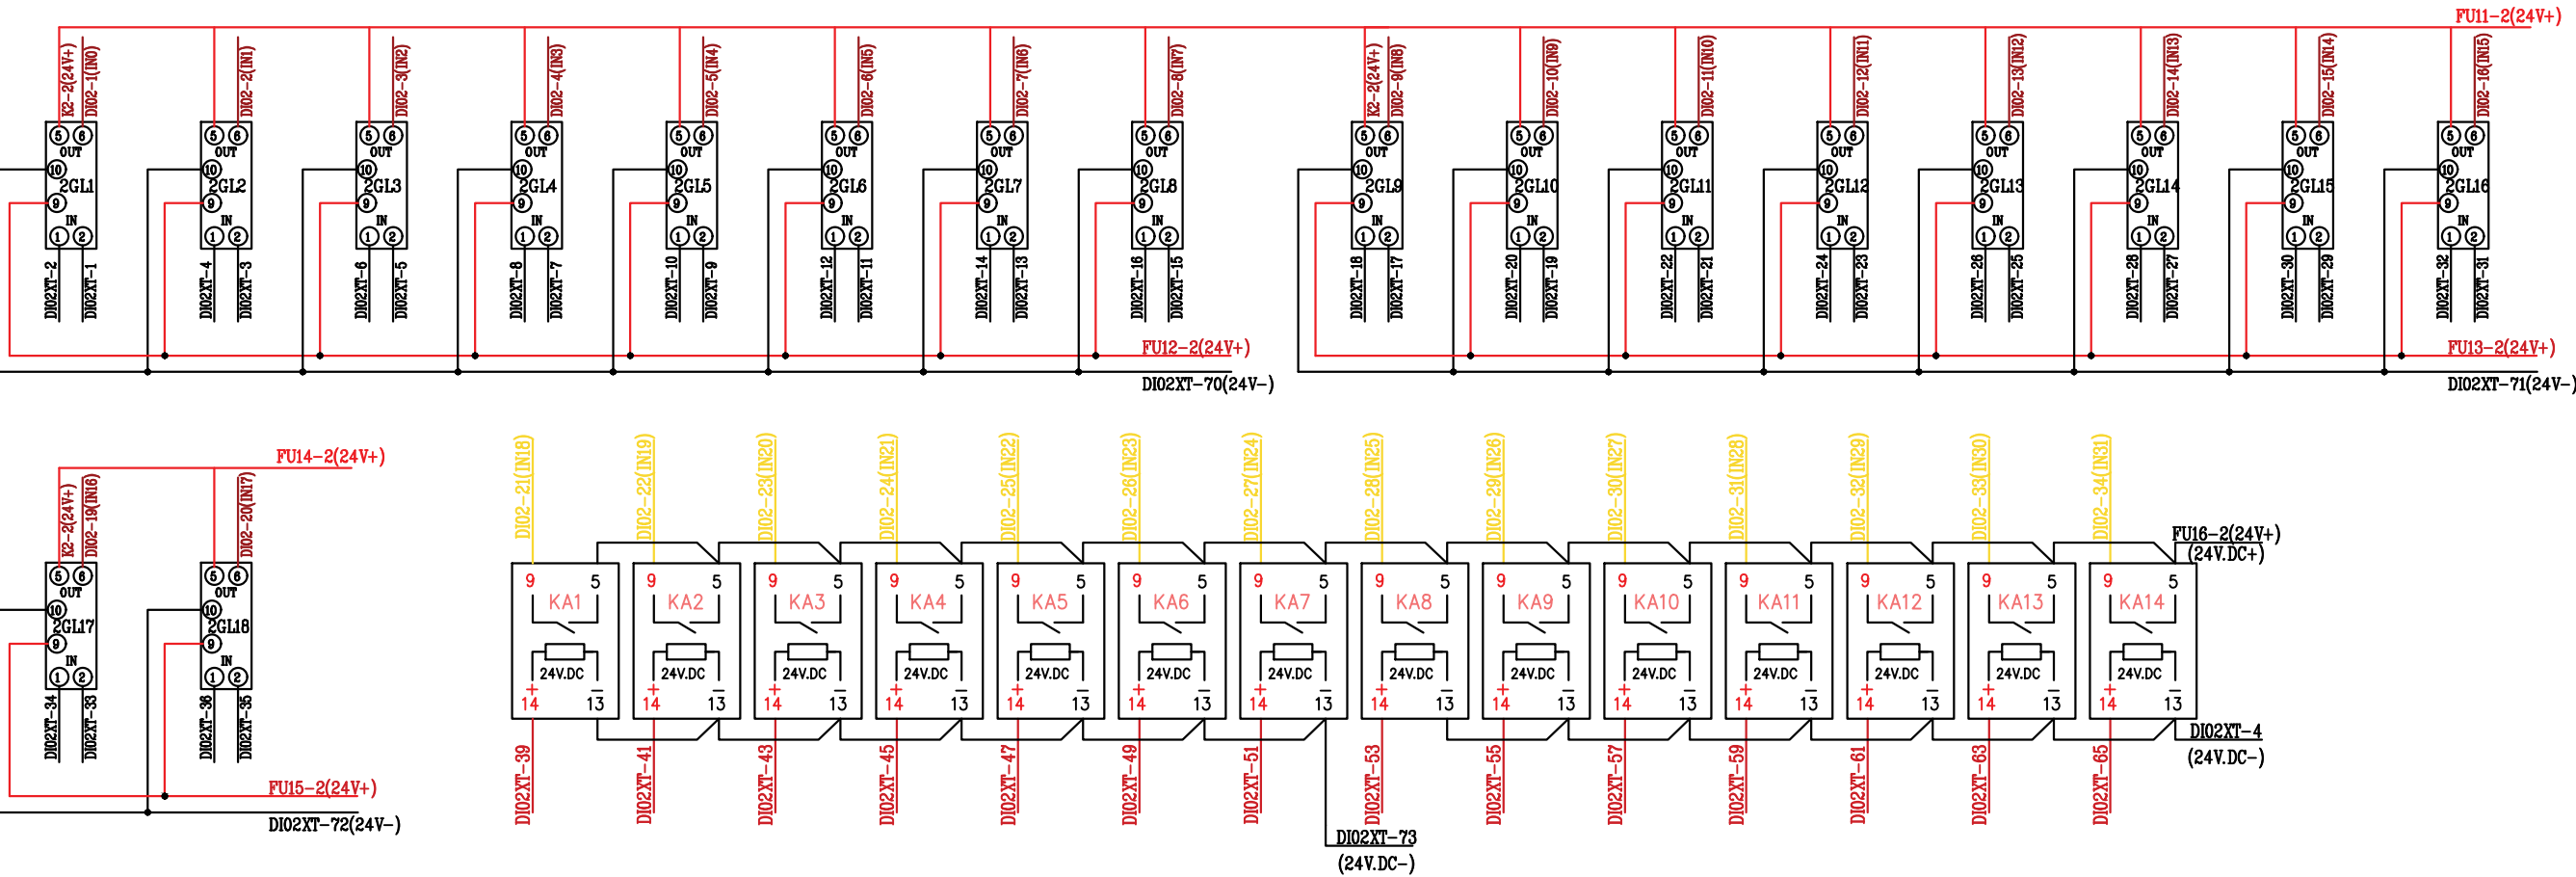

DI02			
1756-IB32 DI			
2GL1-2-6	2 IN-1	IN-0	1 2GL1-6
2GL4-6	4 IN-3	IN-2	3 2GL3-6
2GL6-6	6 IN-5	IN-4	5 2GL5-6
2GL8-6	8 IN-7	IN-6	7 2GL7-6
2GL10-6	10 IN-9	IN-8	9 2GL9-6
2GL12-6	12 IN-11	IN-10	11 2GL11-6
2GL14-6	14 IN-13	IN-12	13 2GL13-6
2GL16-6	16 IN-15	IN-14	15 2GL15-6
DI02XT-1	18 GND-0	GND-0	17 DI02XT-36
2GL18-6	20 IN-17	IN-16	19 2GL17-6
KA2-9	22 IN-19	IN-18	21 KA1-9
KA4-9	24 IN-21	IN-20	23 KA3-9
KA6-9	26 IN-23	IN-22	25 KA5-9
KA8-9	28 IN-25	IN-24	27 KA7-9
KA10-9	30 IN-27	IN-26	29 KA9-9
KA12-9	32 IN-29	IN-28	31 KA11-9
KA14-9	34 IN-31	IN-30	33 KA13-9
DI02XT-3	36 GND-1	GND-1	35 DI02XT-38

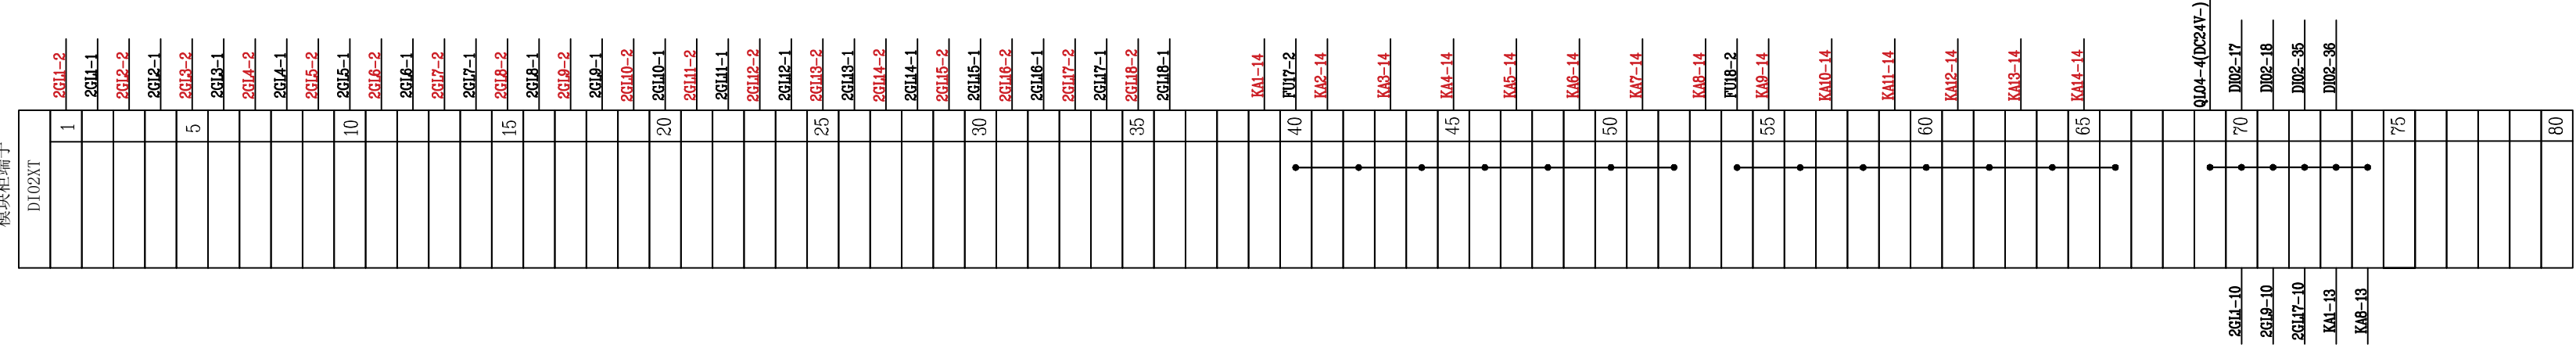


模块型号	柜号	机架号	槽号	类型
1756-IB32	abPLC	1	3	DI

注：2GLxx代表开关量信号隔离器，外接开关量信号需要是无源干节点信号。

客户名称			长沙智宸自动化设备有限责任公司
客户工程编号			
客户图号			
审定	设计部门	工程	首衡京唐钢铁联合有限责任公司炼铁作业部PLC项目
组审	设计专业	名称	
校审	设计阶段	子项名称	abPLC系统
设计	比例 1:100	图纸名称	DI02模块接线图
完成日期 2026/03	图幅 1.5A2	图号	-6

模块型号	柜号	机架号	槽号	类型
1756-0B32	abPLC	1	5	D0

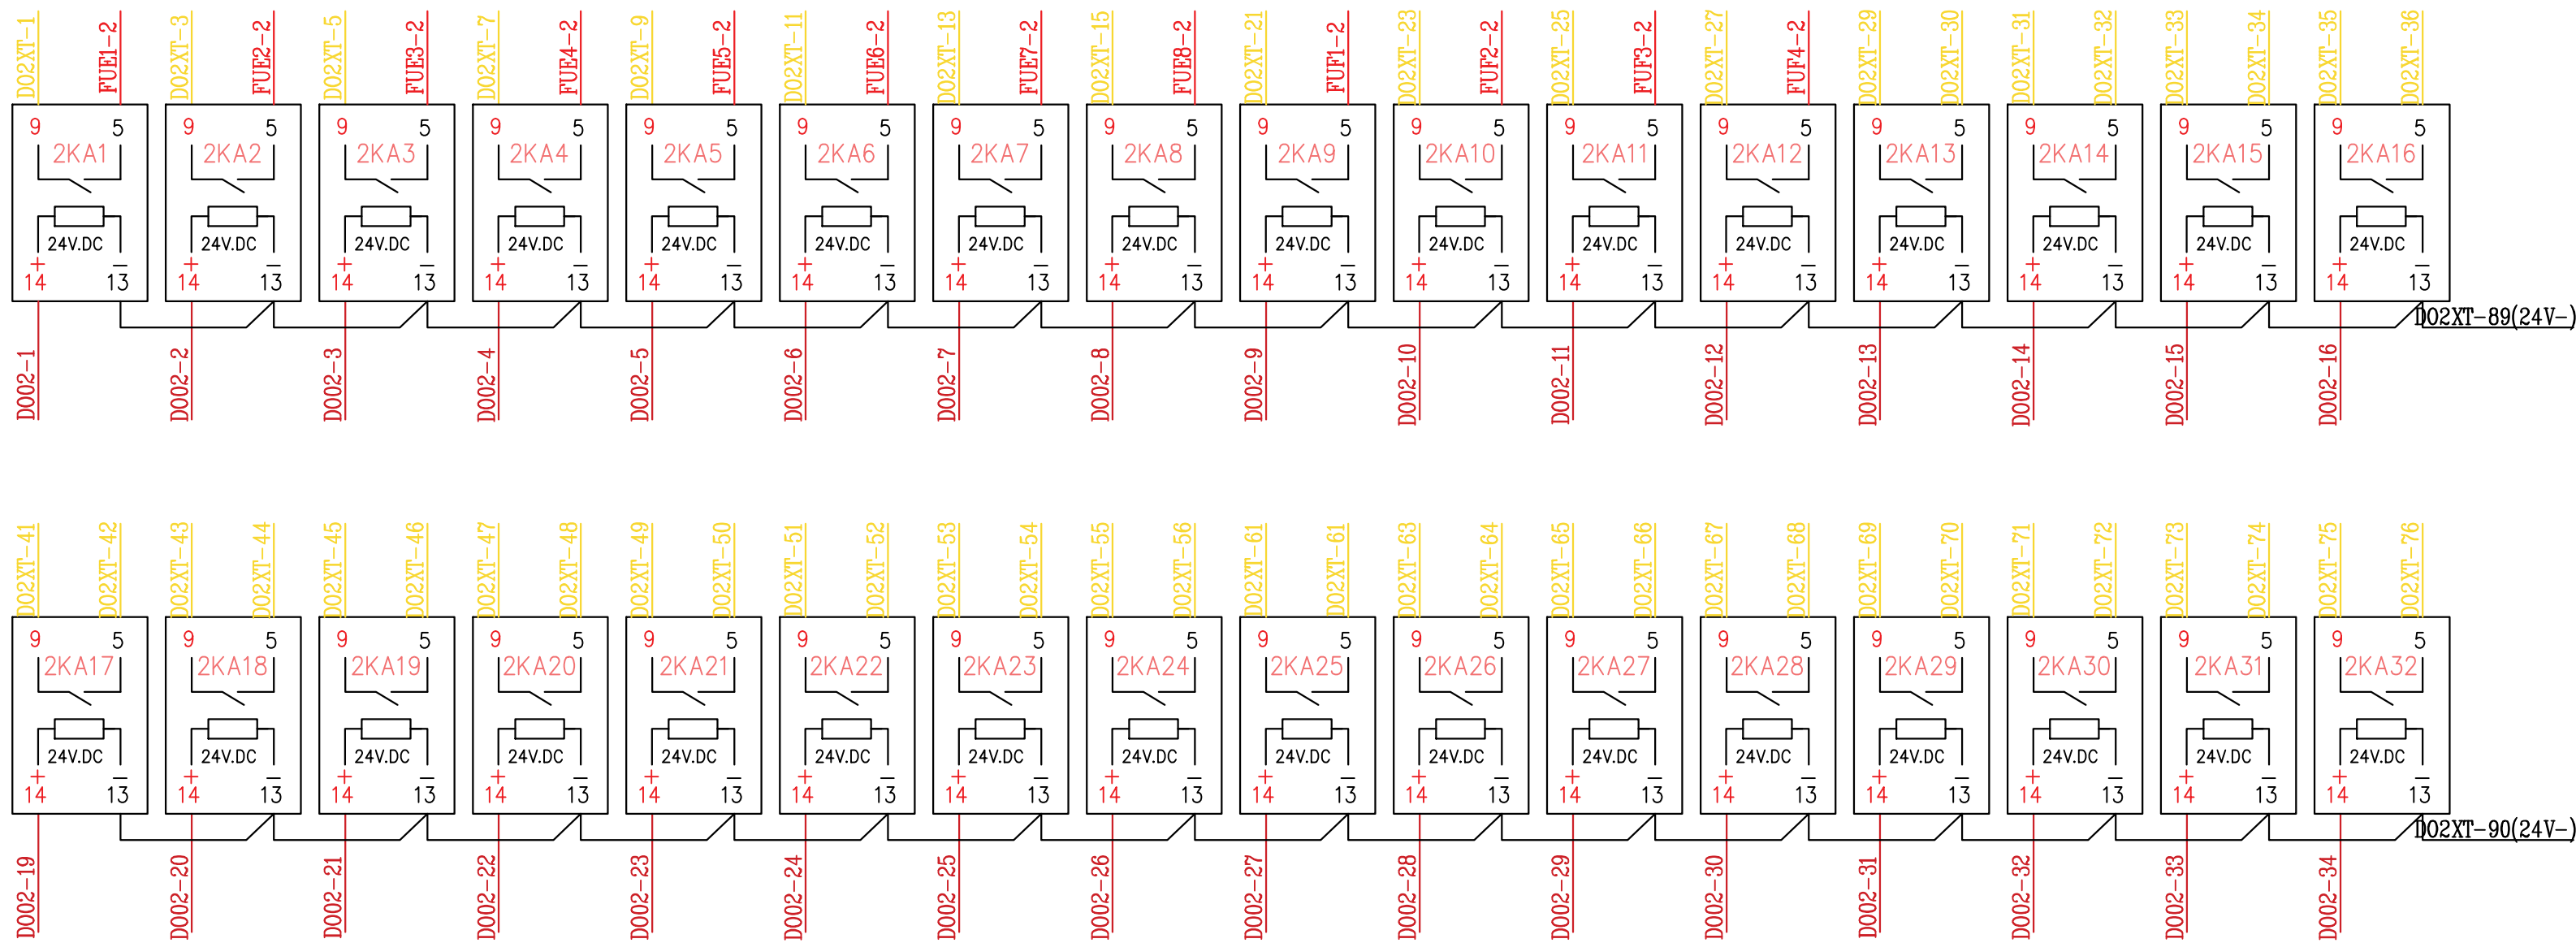


D002

1756-0B32 D0

2KA2-14	2	OUT-1	OUT-0	1	2KA1-14
2KA4-14	4	OUT-3	OUT-2	3	2KA3-14
2KA6-14	6	OUT-5	OUT-4	5	2KA5-14
2KA8-14	8	OUT-7	OUT-6	7	2KA7-14
2KA10-14	10	OUT-9	OUT-8	9	2KA9-14
2KA12-14	12	OUT-11	OUT-10	11	2KA11-14
2KA14-14	14	OUT-13	OUT-12	13	2KA13-14
2KA16-14	16	OUT-15	OUT-14	15	2KA15-14
D02XT-82	18	DC-0(+)	RTN OUT-0	17	D02XT-87
2KA18-14	20	OUT-17	OUT-16	19	2KA17-14
2KA20-14	22	OUT-19	OUT-18	21	2KA19-14
2KA22-14	24	OUT-21	OUT-20	23	2KA21-14
2KA24-14	26	OUT-23	OUT-22	25	2KA23-14
2KA26-14	28	OUT-25	OUT-24	27	2KA25-14
2KA28-14	30	OUT-27	OUT-26	29	2KA27-14
2KA30-14	32	OUT-29	OUT-28	31	2KA29-14
2KA32-14	34	OUT-31	OUT-30	33	2KA31-14
D02XT-83	36	DC-1(+)	RTN OUT-1	35	D02XT-88


32 点数字量输出模块

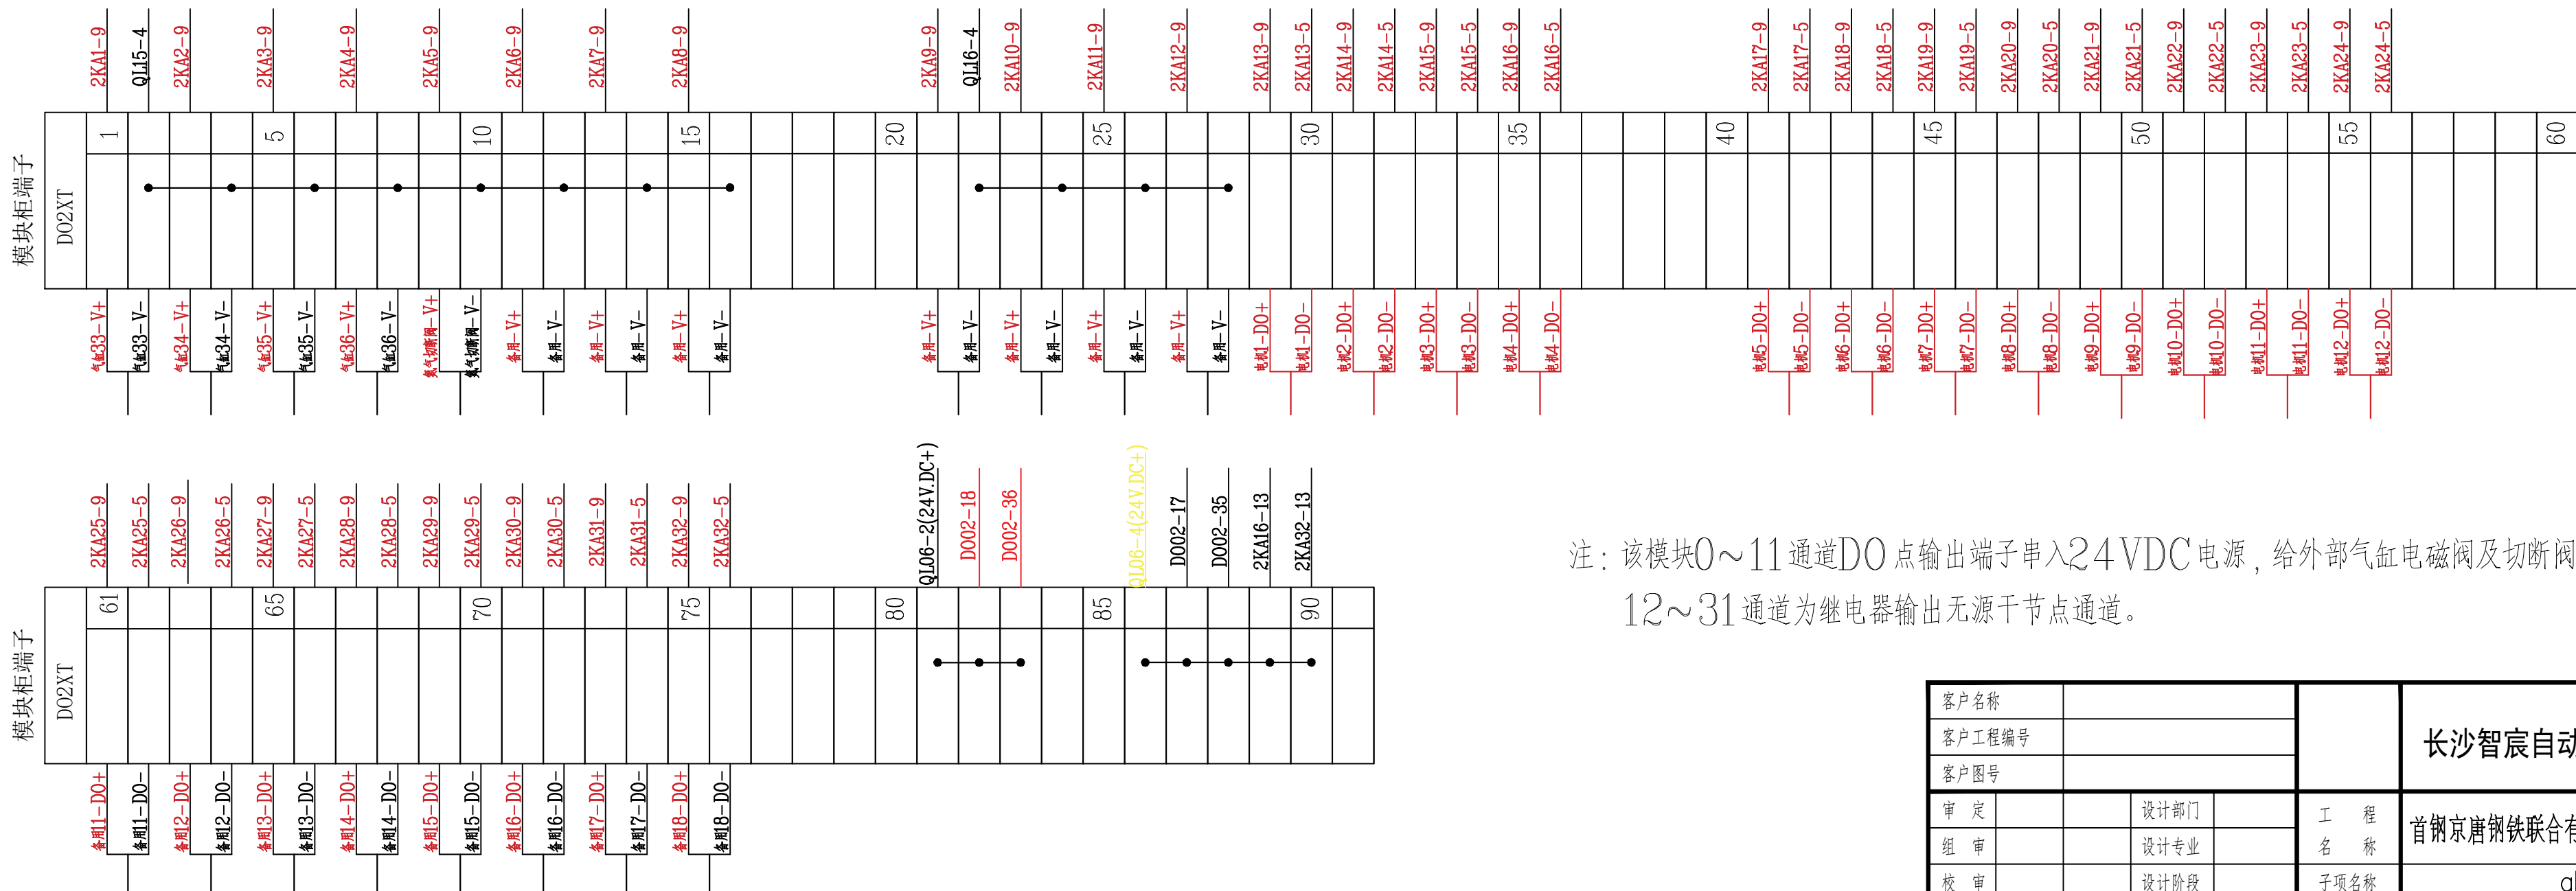


注：该模块0~11通道DO点输出端子串入24VDC电源，给外部气缸电磁阀及切断阀供电。
12~31通道为继电器输出无源干节点通道。

客户名称				长沙智宸自动化设备有限责任公司	
客户工程编号					
客户图号					
审 定		设计部门		工 程 名 称	首钢京唐钢铁联合有限责任公司炼铁作业部PLC项目
组 审		设计专业			
校 审		设计阶段		子项名称	abPLC系统
设 计		比 例	1:100	图纸名称	DO01模块接线图
完成日期	2026/03	图 幅	A2	图 号	-8
				版次	

模块型号	柜号	机架号	槽号	类型
1756-0F4	abPLC	1	7	AO

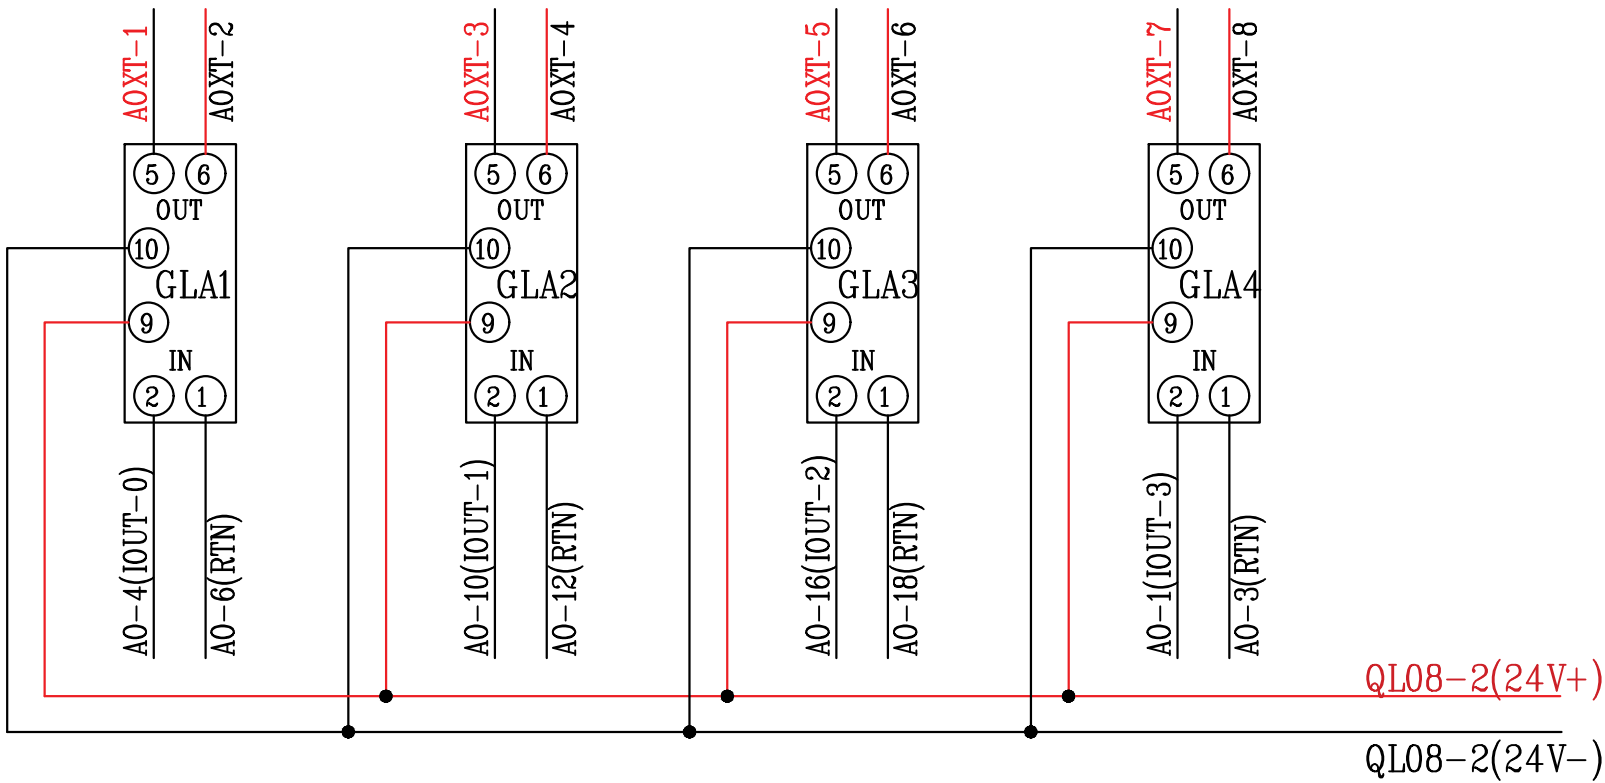

模块柜端子		GLA1-5	GLA1-6	GLA2-5	GLA2-6	GLA3-5	GLA3-6	GLA4-5	GLA4-6	
AOXT	1					5				10
	+									
	-									
	+									
	-									
	+									
	-									
		调节阀+	调节阀-							
		阀位给定								

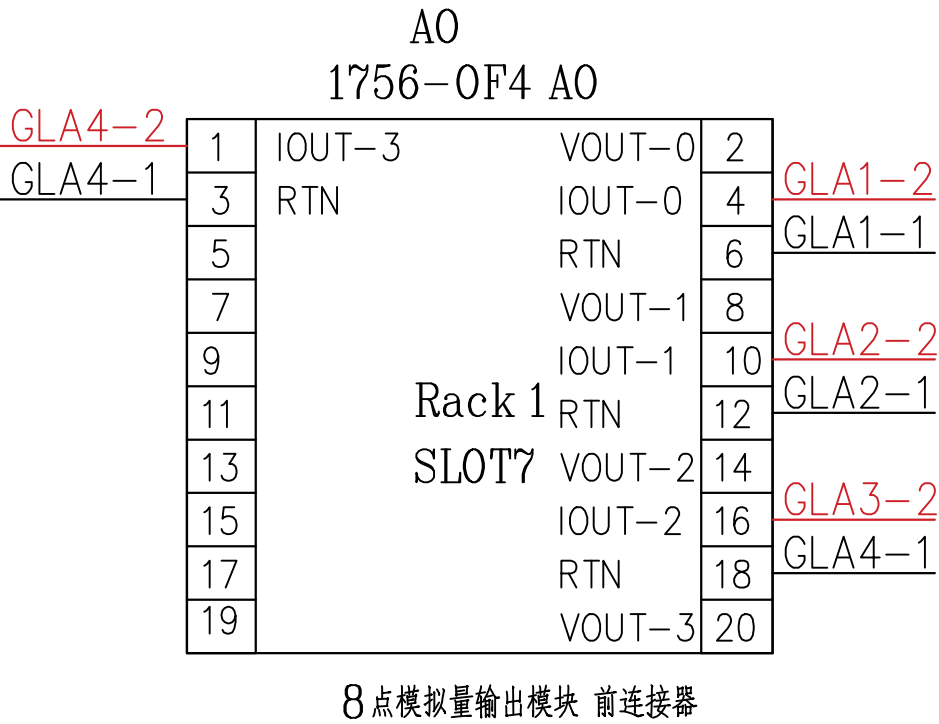

注：GLA代表模拟量隔离器。

客户名称			长沙智宸自动化设备有限责任公司
客户工程编号			
客户图号			
审 定		设计部门	工 程 名
组 审		设计专业	首钢京唐钢铁联合有限责任公司炼铁作业部PLC项目
校 审		设计阶段	abPLC系统
设 计		比 例	图纸名称
完成日期		图 幅	图 号
			-10
			版次